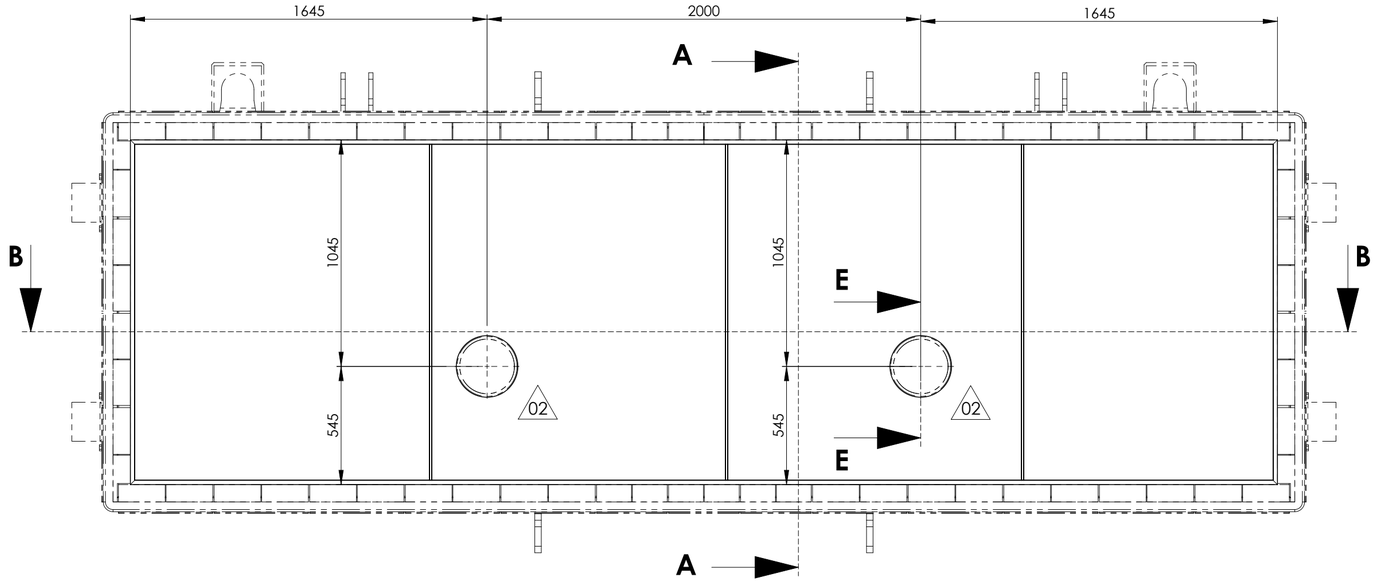

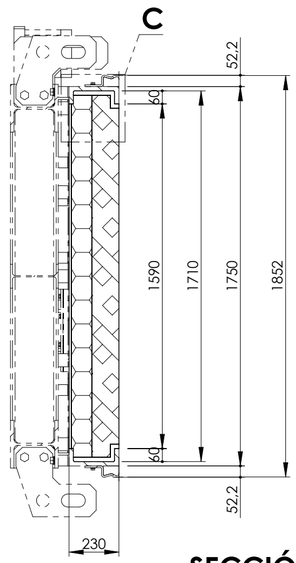

SECCIÓN A-A

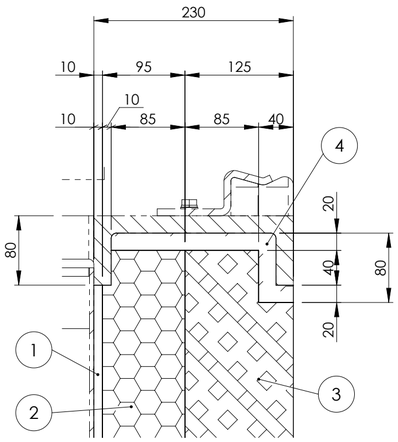

DETALLE C

ESCALA (1 : 5)

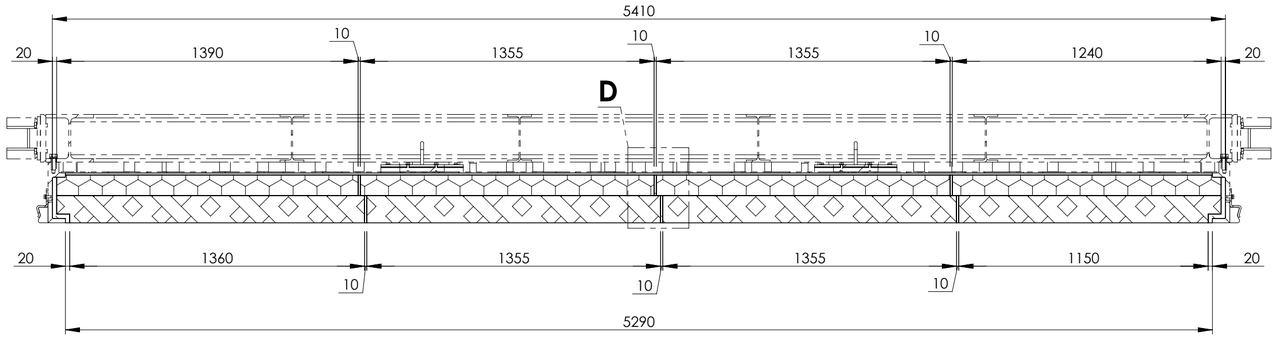

SECCIÓN B-B

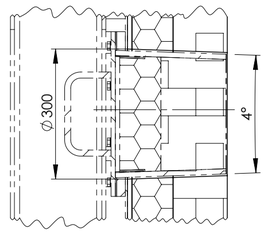

SECCIÓN E-E

ESCALA (1 : 10) 02

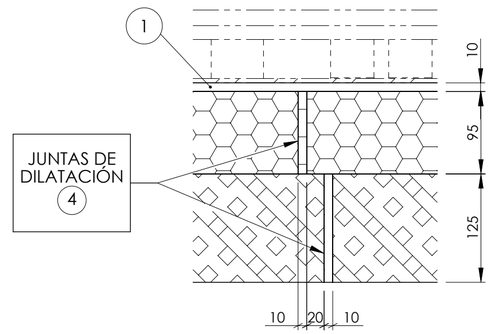

DETALLE D

ESCALA (1 : 5)

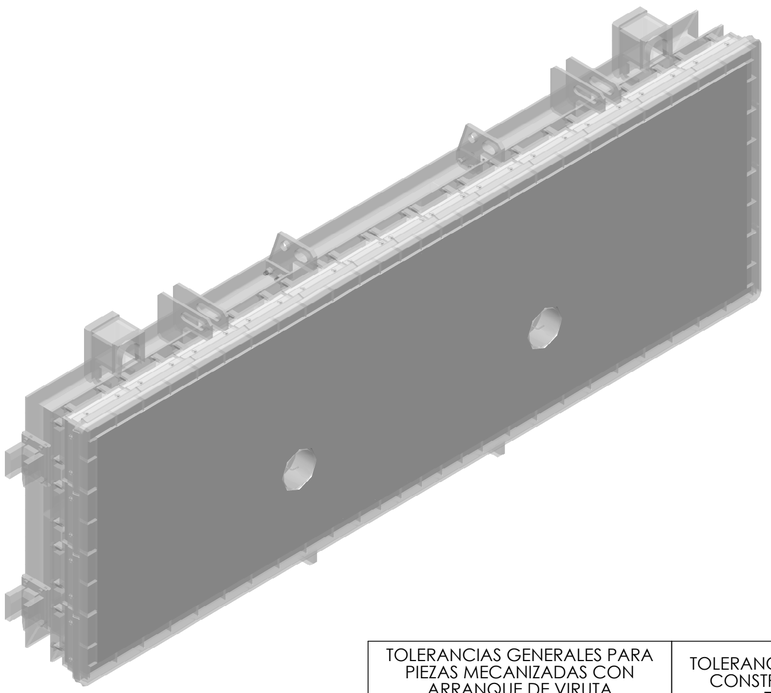

LAS CANTIDADES DE LOS MATERIALES QUE APARECEN EN LA LISTA SON CANTIDADES TEÓRICAS SIN NINGUNA DEMASÍA

IMPREGNAR CARAS DE PLACA INSULFRAX ESPESOR 10 mm. (MARCA 1) EN CONTACTO CON EL HORMIGÓN, CON **PLASTICOAT A-500**.

MARCA	CODIGO	DESCRIPCION	Nº P	CANT. UNITARIA	CANT. TOTAL	UN	ANCHO	LARGO
4	55D00007	MANTA BIO 1200 GR 25 128 KG/M3 CE/97/69 (610X7320 MM) FIBRA VITREA BIOSOLUBLE SILICE-CALCIO-MAGNESIA	5	1	5	MT2		
3	56D00006	HORMIGON CALDE CAST LF 44 (ANTES PHLOX 1500 C SR)	1	2311	2311	KGR		
2	56E00000	HORMIGON LW MIX 124 C/G CALDECAST	1	787	787	KGR		
1	55D00034	PLACA AISLANTE 10MM 1200ºC BIOSOLUBLE 1250X1000 INSULFRAX 110LD - UNIFRAX-	9	1	9	MT2		

01 01

REV. Nº	CONCEPTO	FECHA	NOMBRE
1	ACTUALIZACION DEL PESO DEL HORMIGON PHLOX & CALDECAST MARCAS 2 & 3	24/01/2023	Distek1
2	INSERCION DE AGUJEROS PARA AMARRE QUEMADOR	01/03/2023	Distek1

TOLERANCIAS GENERALES PARA PIEZAS MECANIZADAS CON ARRANQUE DE VIRUTA
DIN-7168
GRADO DE PRECISION: m-S

TOLERANCIAS GENERALES PARA CONSTRUCCION SOLDADA
DIN-8570
GRADO DE PRECISION: AE

NOTA IMPORTANTE:
TODAS LAS SOLDADURAS NO INDICADAS, SE HARAN CON CORDON CONTINUO CON GARGANTA **a** (UNE-EN ISO 2553) DE 0,4 EL ESPESOR MINIMO A UNIR, CUANDO SE SUELDE POR LOS DOS LADOS( ), Y DE 0,7 EL ESPESOR MINIMO A UNIR CUANDO SE SUELDE SOLO POR UNO. ( )

NO TOMAR MEDIDAS A ESCALA.
EN CASO DE DUDA O PRECISAR COTAS ADICIONALES, CONTACTAR CON NUESTRO DEPARTAMENTO DE INGENIERIA.

	FECHA	NOMBRE
DIBUJADO	23/06/2022	Distek1
COMPROBADO	02/03/2023	psrra
SUPERVISADO		

ghi SMART FURNACES
Barrio de Aperribay, 4
48960 Galdakao (Bizkaia)
Teléfono: (+34) 944 49 16 00
www.ghihornos.com

ESCALA 1:20
PESO (KG) 3132.32
DENOMINACION: REVESTIMIENTO PUERTA DE CARGA
INSTALACION: RAN
Nº: S06-01-08-PGG-0220-008 | REV. 2 | FORMATO: A2 | HOJA: 1 DE 1

ESTE PLANO ES PROPIEDAD DE GHI HORNOS INDUSTRIALES Y ES CONFIDENCIAL. - NO DEBE SER CEDIDO, COPIADO NI COMUNICADO DE CUALQUIER OTRA FORMA A TERCEROS SIN PERMISO ESCRITO